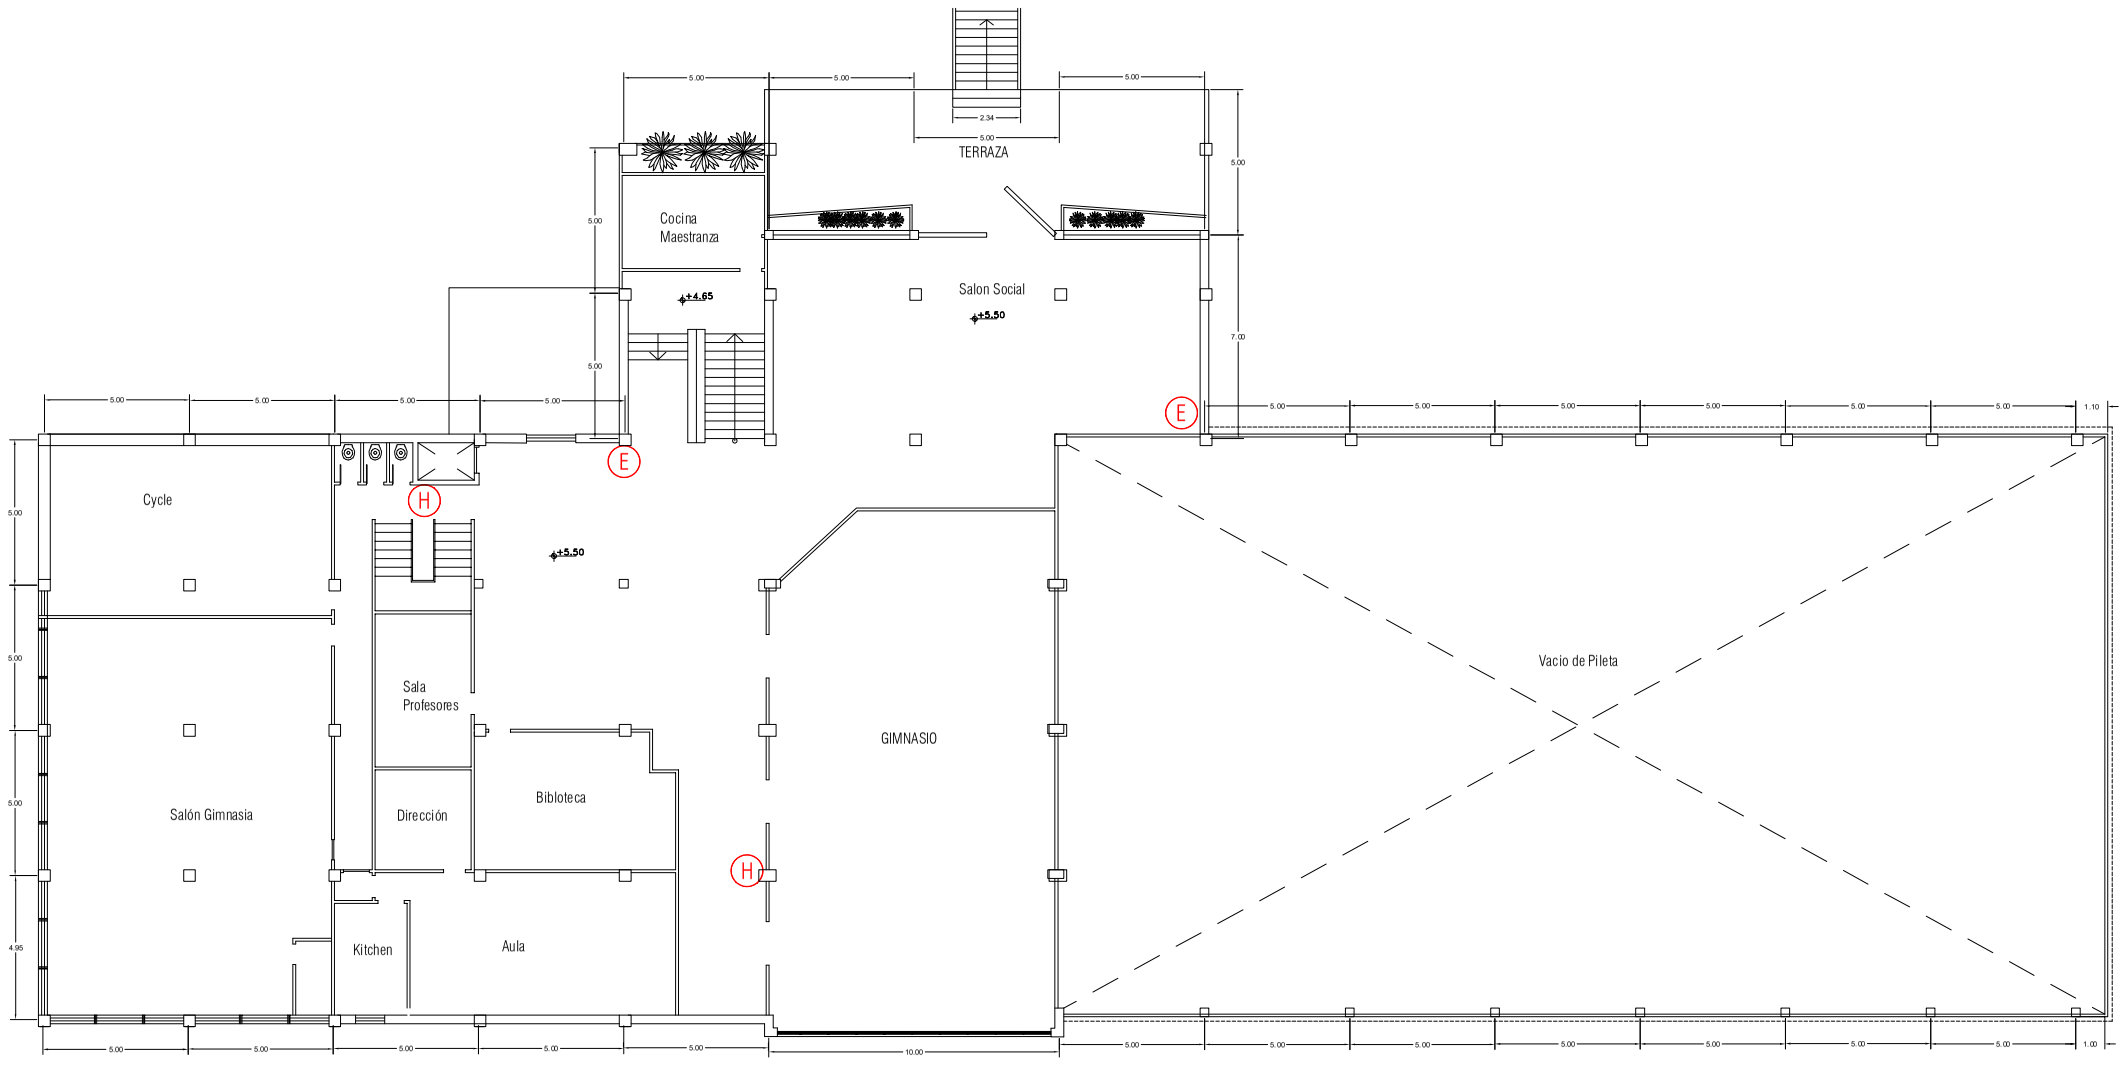

PLANO PRIMER PISO

REFERENCIAS ELEMENTOS CONTRA INDENDIOS

(E) Extintor "ABC"

(H) Bocas de Hidrantes

PLANO INSTALACIONES CONTRA INCENDIO

RUBRO: ESPECTÁCULOS Y DIVERSIONES PÚBLICAS NATATORIO

TITULAR:

ASOCIACIÓN CRISTIANA DE JOVENES DE LA REPUBLICA ARGENTINA

CALLE: AV. LA FUENTE 2480 - PRIMER PISO

C: 1 S: 60 M: 72 D fraccion : D

ESCALA : 1:100

UBICACIÓN

SUP. TOTAL DE PRIMER PISO 1676m2

SUP. PARCELA:

SUP. HABILITACIÓN:

TITULAR: ASOCIACIÓN CRISTIANA DE JOVENES DE LA REPUBLICA ARGENTINA
EDUARDO J. RODRIGUEZ (APODERADO)
DOM. RECONQUISTA 435 - CAP

Profesional: Federico Javier Varela
Mat. Prof.: CPAU 19220
DNI.: 18.392.483